

United Nations Development Programme

Request For Expression of Interest (REOI)

[UNDP-REOI-2026-.....]

Request for Expression of Interest for Registration of Contractors for Training Programme on Veneer House Construction

UNDP Sri Lanka invites interested Construction Companies (Contractors) to submit Expressions of Interest (EOI) in respect of the requirements described below. The purpose of this EOI is to identify eligible contractors that wish to register for and participate in the mandatory Training Programme on Veneer House Construction and, subject to the requirements of the forthcoming solicitation, participate in the subsequent procurement process for the proposed Veneer House construction works.

Deadline for the Submission/Registration of EOI: 12:00 noon (Sri Lanka Standard Time), 3 October 2026

Registration Link: <https://forms.gle/YKftyPLdGBjYgEZRA>

Contact Person for correspondence and clarifications: A. C. Ranathunga, Field Engineer, UNDP Sri Lanka - +94772546840, Champika.ranathunga@undp.org

1. Background

The United Nations Development Programme (UNDP), under the project “Disaster Waste Clearance and Rehabilitation of Community Facilities through a Participatory Approach in Cyclone-Affected Communities,” plans to construct 18 Veneer Houses at selected locations in the Central Province of Sri Lanka.

The proposed buildings will adopt an improved plywood-based construction technology introduced with the technical support of a Japanese Expert Team, with particular emphasis on rapid, practical and resilient construction. In addition to supporting the planned construction activities, the initiative seeks to transfer and disseminate knowledge and practical skills related to Veneer House construction among Sri Lankan contractors. This will contribute to strengthening local construction capacity, particularly in disaster-affected and disaster-prone areas where rapid construction of community facilities and other essential buildings may be required following disasters and emergencies.

2. Scope of Work

In preparation for the proposed construction works, UNDP will conduct a specialized one-day Training Programme on Veneer House Construction under the technical guidance of a Japanese Expert Team. All contractors intending to participate in the subsequent procurement process for the construction of Veneer Houses are required to participate in this training programme.

During the programme, the Japanese Expert Team, together with the UNDP technical team, will provide technical and practical guidance covering:

- Veneer House construction methodology, construction sequence and key construction techniques;
- interpretation of typical designs, drawings and construction details;
- material requirements and relevant workmanship considerations; and
- relevant aspects of the Bill of Quantities (BOQ) and implementation requirements.

Date	10 October 2026
Time	9:00 a.m. - 2:00 p.m.
Venue	Kandy City
Resource Team	Japanese Expert Team / Consultants together with the UNDP technical team

3. Purpose of the EOI

The purpose of this EOI is to assess the interest of potential contractors in the upcoming Veneer House construction works and to register eligible contractors for the mandatory project-specific training programme.

Interested Contractors are invited to express their interest and provide information regarding their registration, qualifications, relevant experience and proposed participant(s) for the training.

Important: Only contractors who successfully register for and participate in the above training programme will be eligible to participate in the subsequent bidding/procurement process for the proposed Veneer House construction works under the project, subject to the eligibility, qualification and other requirements specified in the formal solicitation documents issued by UNDP.

The construction of the **18 Veneer Houses** is planned to be implemented in **two stages**.

Stage 1: A total of six (6) Veneer Houses will be constructed, comprising two (2) units in each of the Kandy, Matale and Nuwara Eliya Districts.

Stage 2: The remaining twelve (12) Veneer Houses will be constructed, comprising four (4) units in each of the three districts.

The construction works will be procured through a **competitive national bidding process**, which is expected to commence following the completion of the Veneer House Construction Training Programme. The detailed bidding requirements, construction packages/lots, eligibility criteria and contractual conditions will be specified in the respective solicitation documents issued by UNDP.

4. EOI Format and Submissions

Interested Contractors should submit/provide the following information through the registration link:

- Company name, registered business address and contact details;
- Name and contact details of the EOI focal point;
- Valid CIDA registration details, including registration number, grade, specialization and validity period;
- Evidence of CIDA Grade C8 or higher with an appropriate specialization relevant to building construction works;
- Brief information on relevant building construction experience; and
- Name(s), designation(s) and contact details of the proposed participant(s) for the training programme.

There will be no reimbursement for any costs incurred by Contractors in the preparation and submission of the above information. Such costs shall be borne by the respective Contractors.

The contractor shall furnish documentary evidence, where requested.

5. Submission Details

Interested Contractors are requested to complete and submit the required information through the registration link provided above on or before the closing date and time of this REOI.

EOIs/registrations received after 12:00 noon (Sri Lanka Standard Time) on 3 October 2026 may not be considered. Contractors failing to provide the required information and evidence may be disregarded.

A typical drawing of the proposed Veneer House is attached as Annex 1 to this REOI for the information and reference of interested Contractors.

6. Clarifications:


Any requests for clarification regarding this Expression of Interest (EOI) and the associated training programme should be submitted to A. C. Ranathunga, Field Engineer, UNDP Sri Lanka - +94772546840, Champika.ranathunga@undp.org no later than 1st October 2026. Responses and/or amendments will be communicated by UNDP through the applicable channel.



7. Disclaimer:


This Request for Expression of Interest does not constitute a solicitation. UNDP reserves the right to change or cancel the requirement at any time during the EOI and/or solicitation process. UNDP also reserves the right to require compliance with additional conditions as and when issuing the final solicitation documents. Submitting a reply to this Request for EOI and/or participating in the training programme does not automatically guarantee receipt of solicitation documents or award of any contract. Any subsequent solicitation will be issued in accordance with the rules and procedures of UNDP.


This EOI does not entail any commitment on the part of UNDP, either financial or otherwise. UNDP reserves the right to accept or reject any or all EOIs without incurring any obligation to the Contractors. Submission of an EOI does not constitute an obligation for UNDP to include a company in a future bidding exercise, nor does it assure that a tender exercise will be undertaken.


Annex 1 - Typical Veneer House Drawing

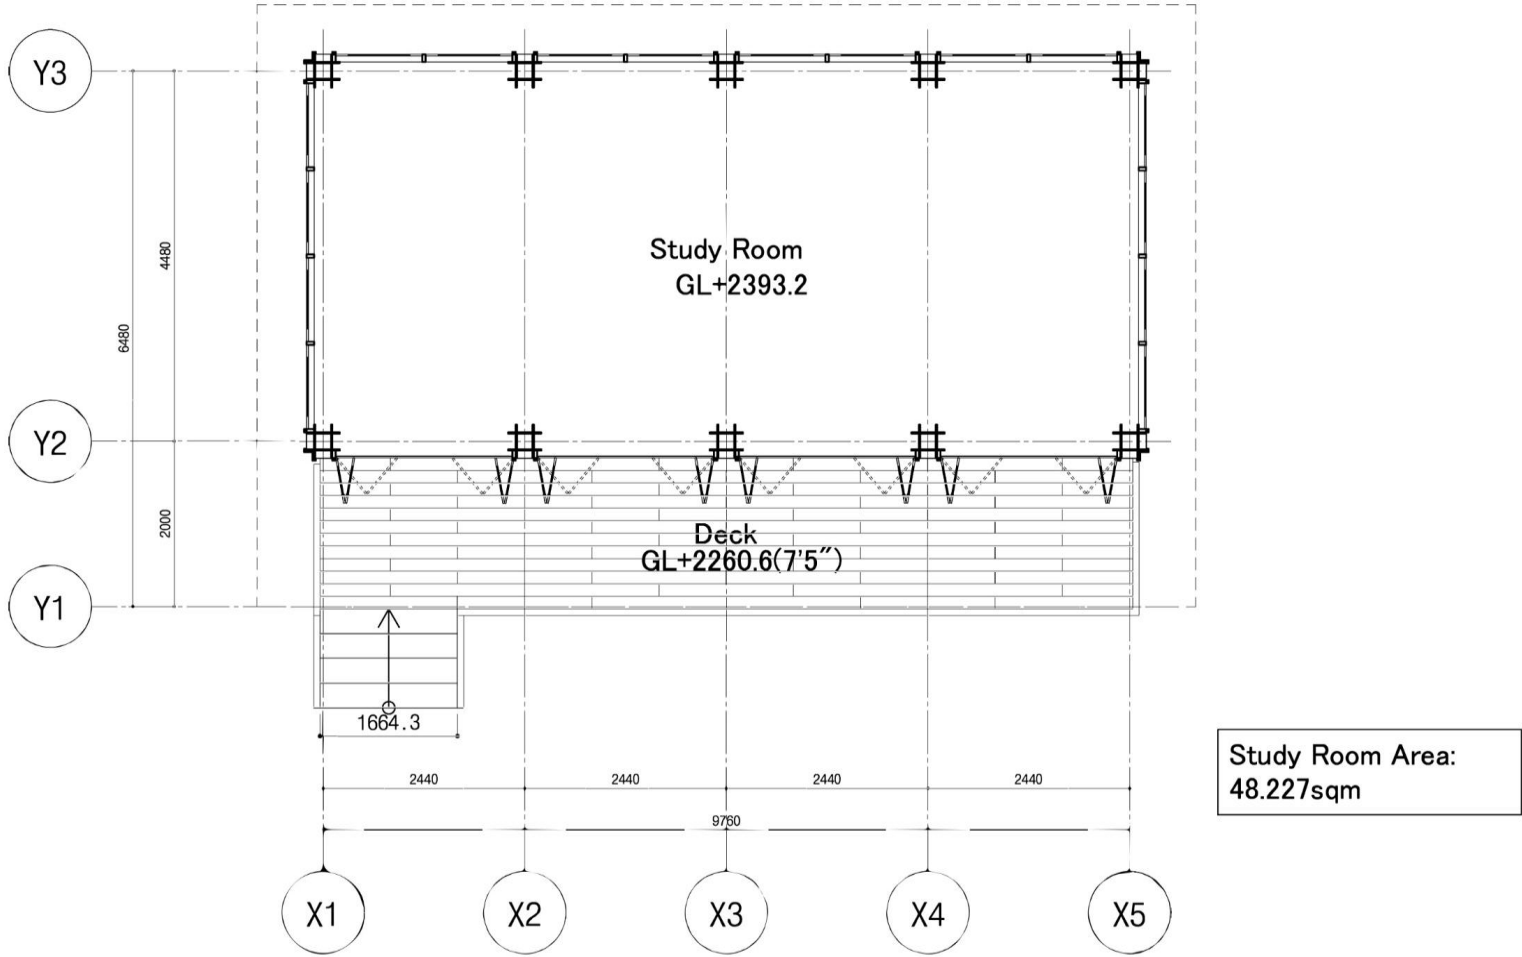


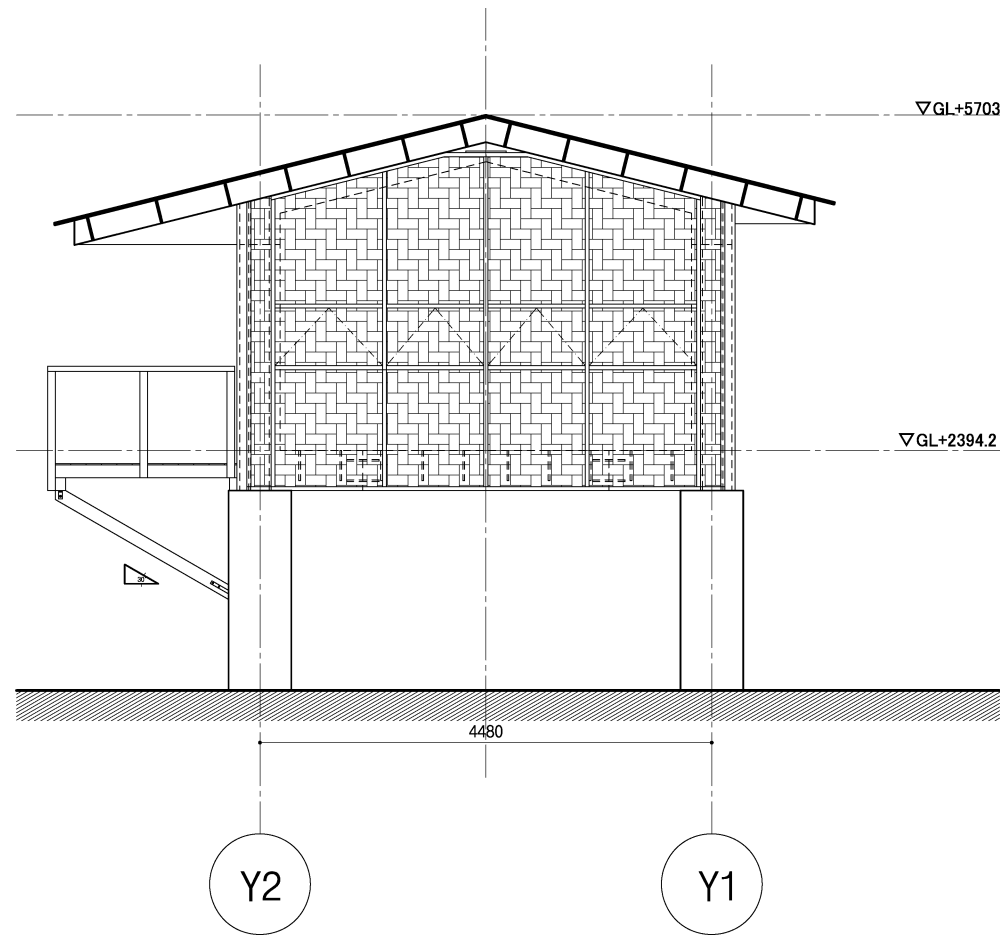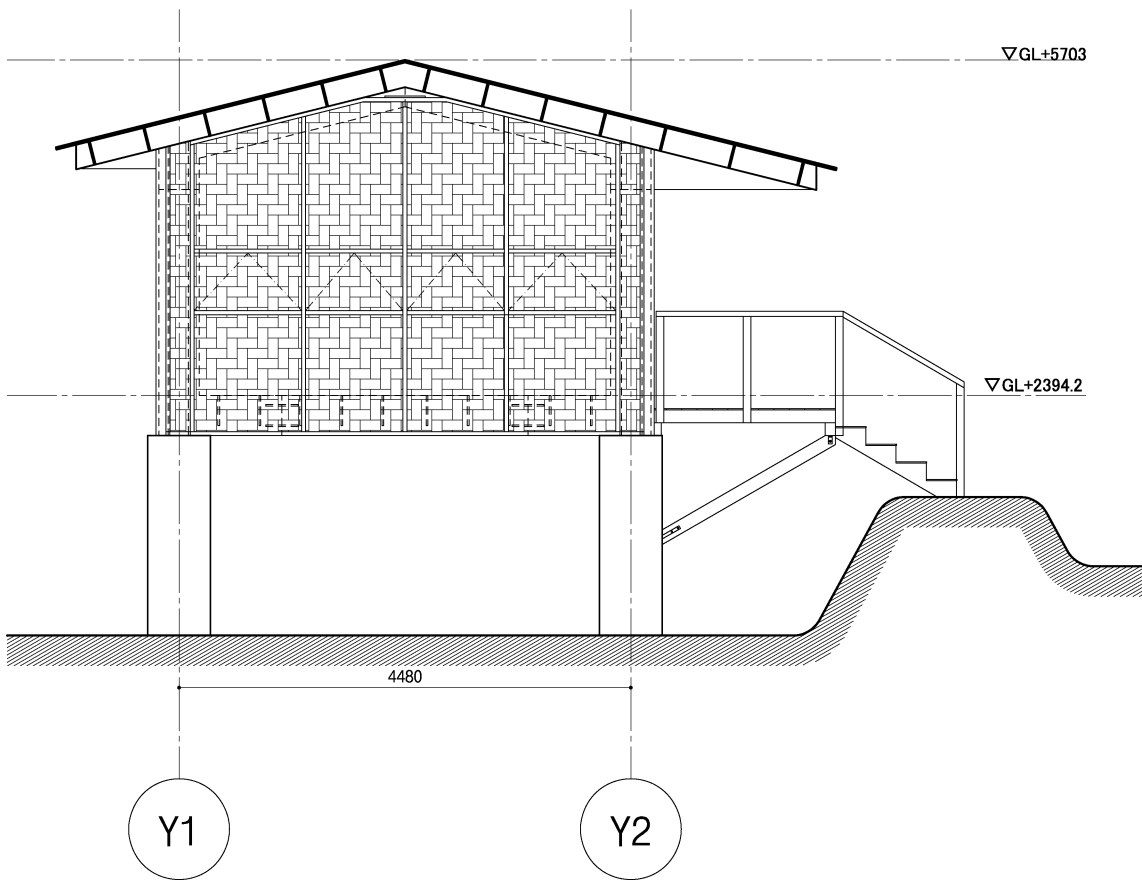


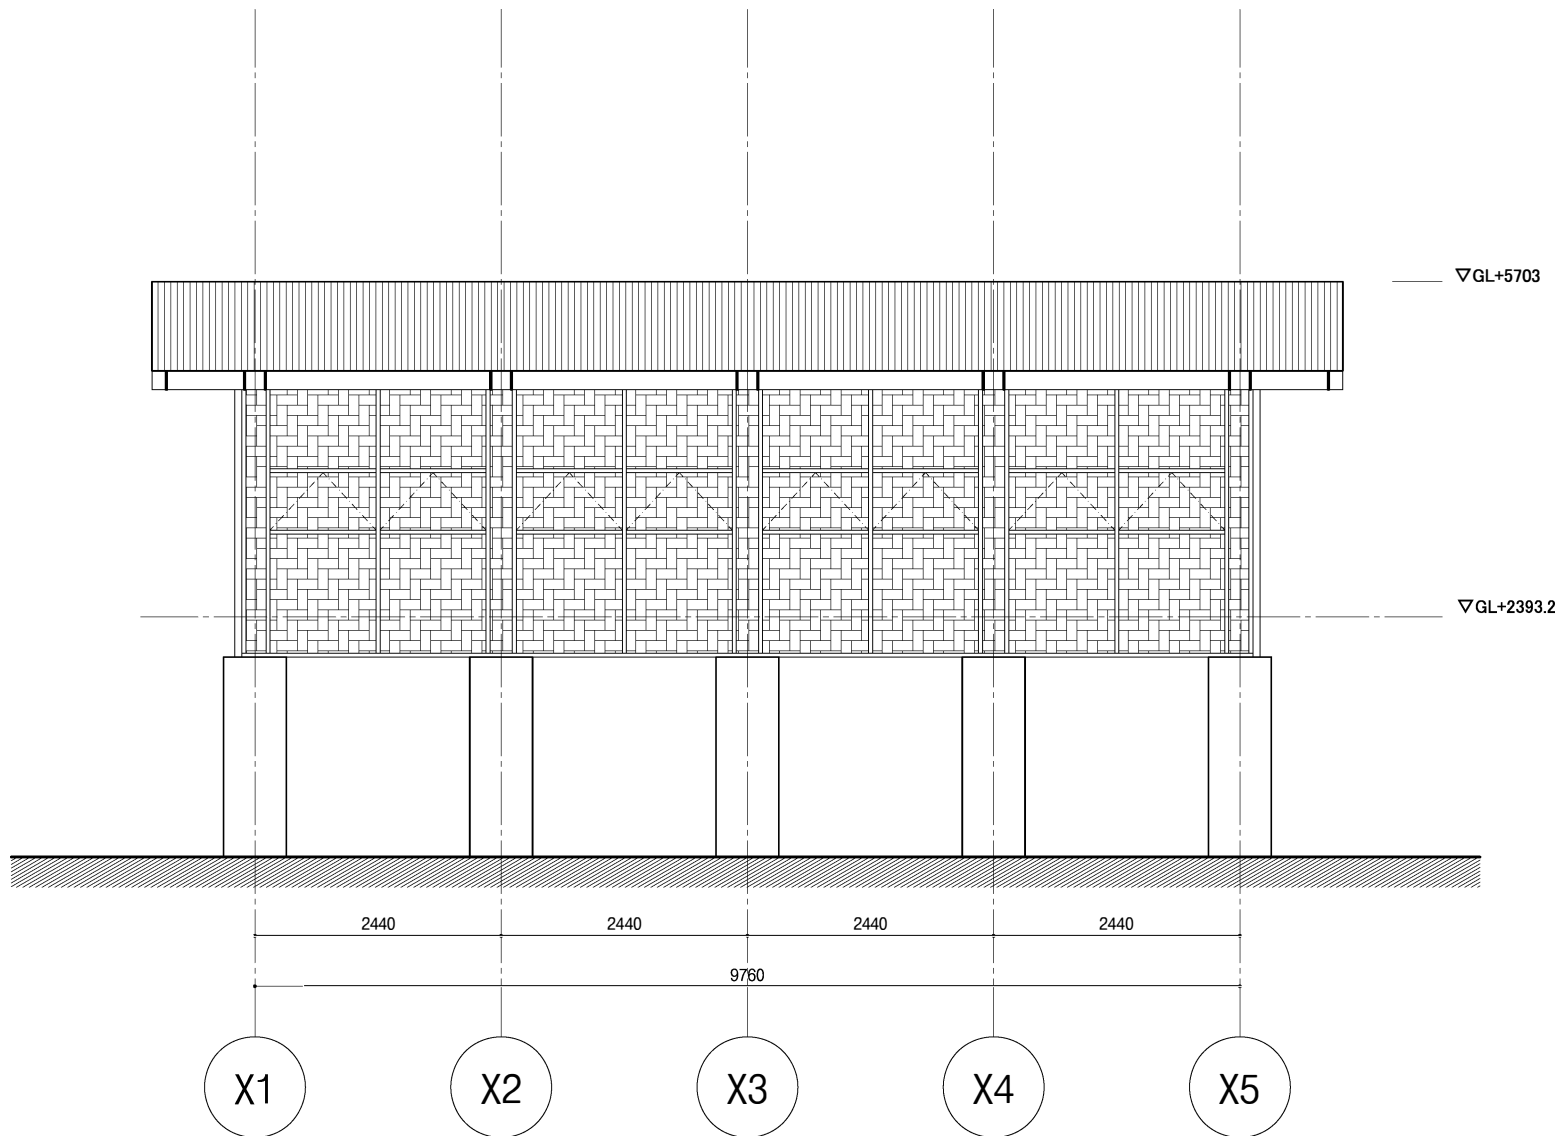


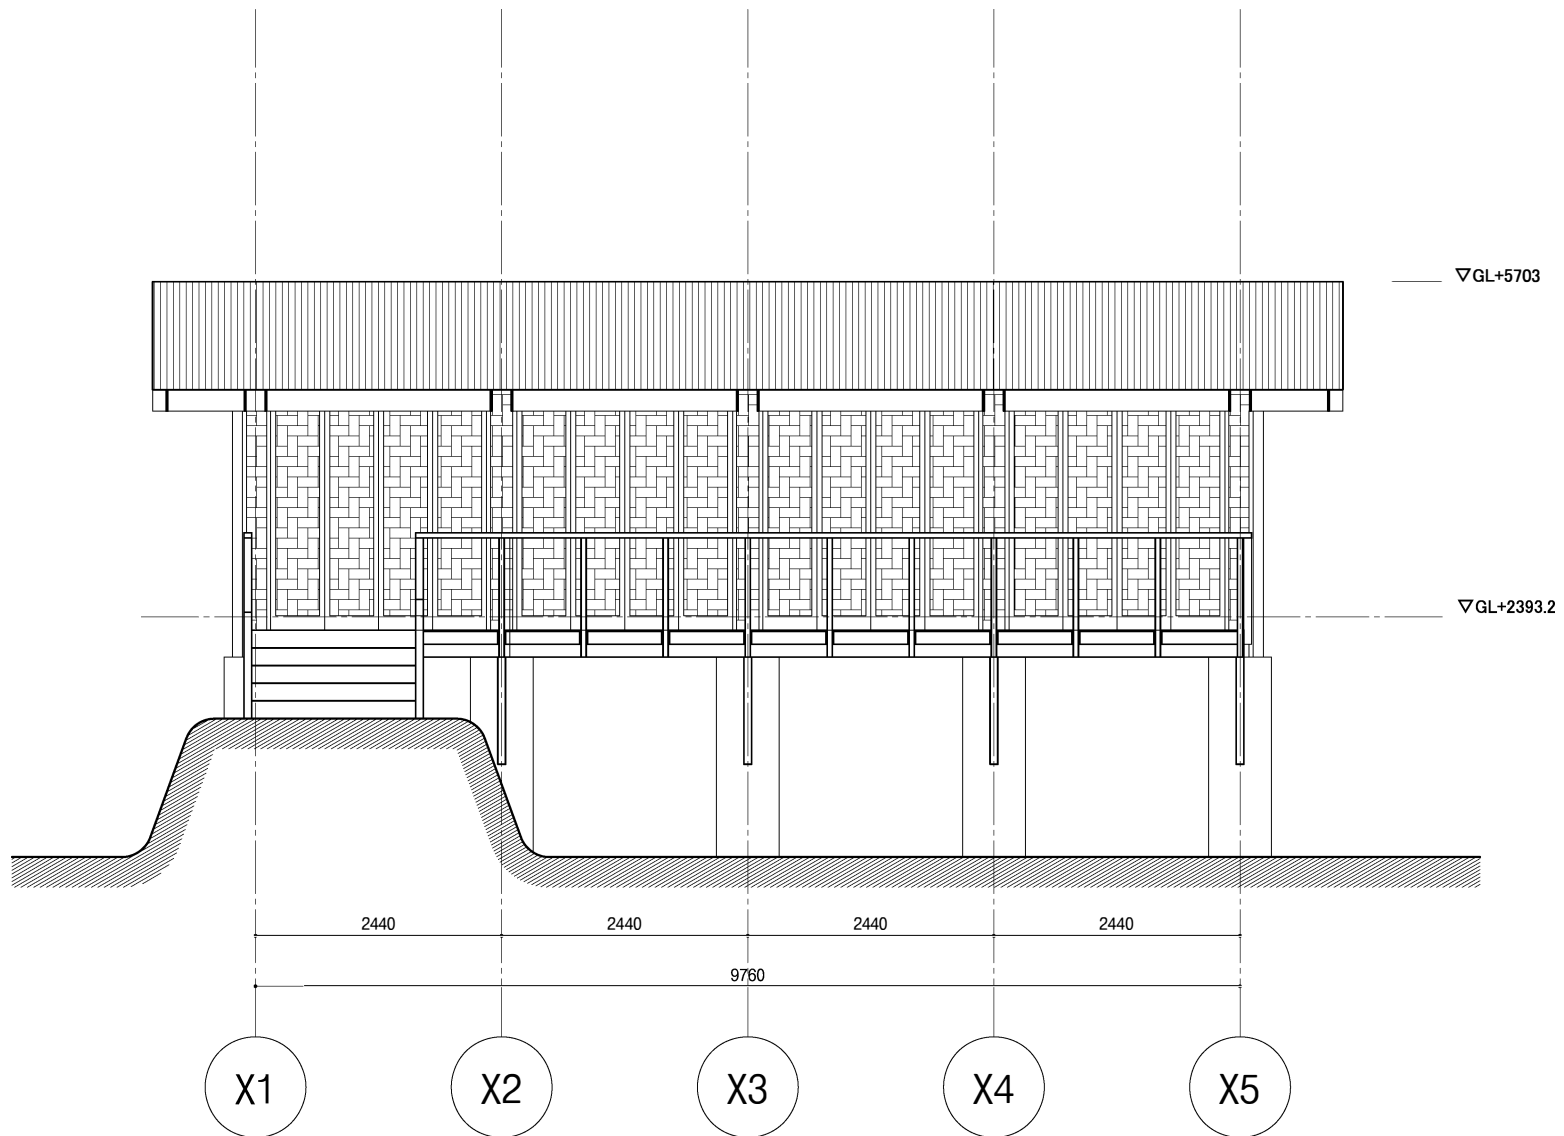

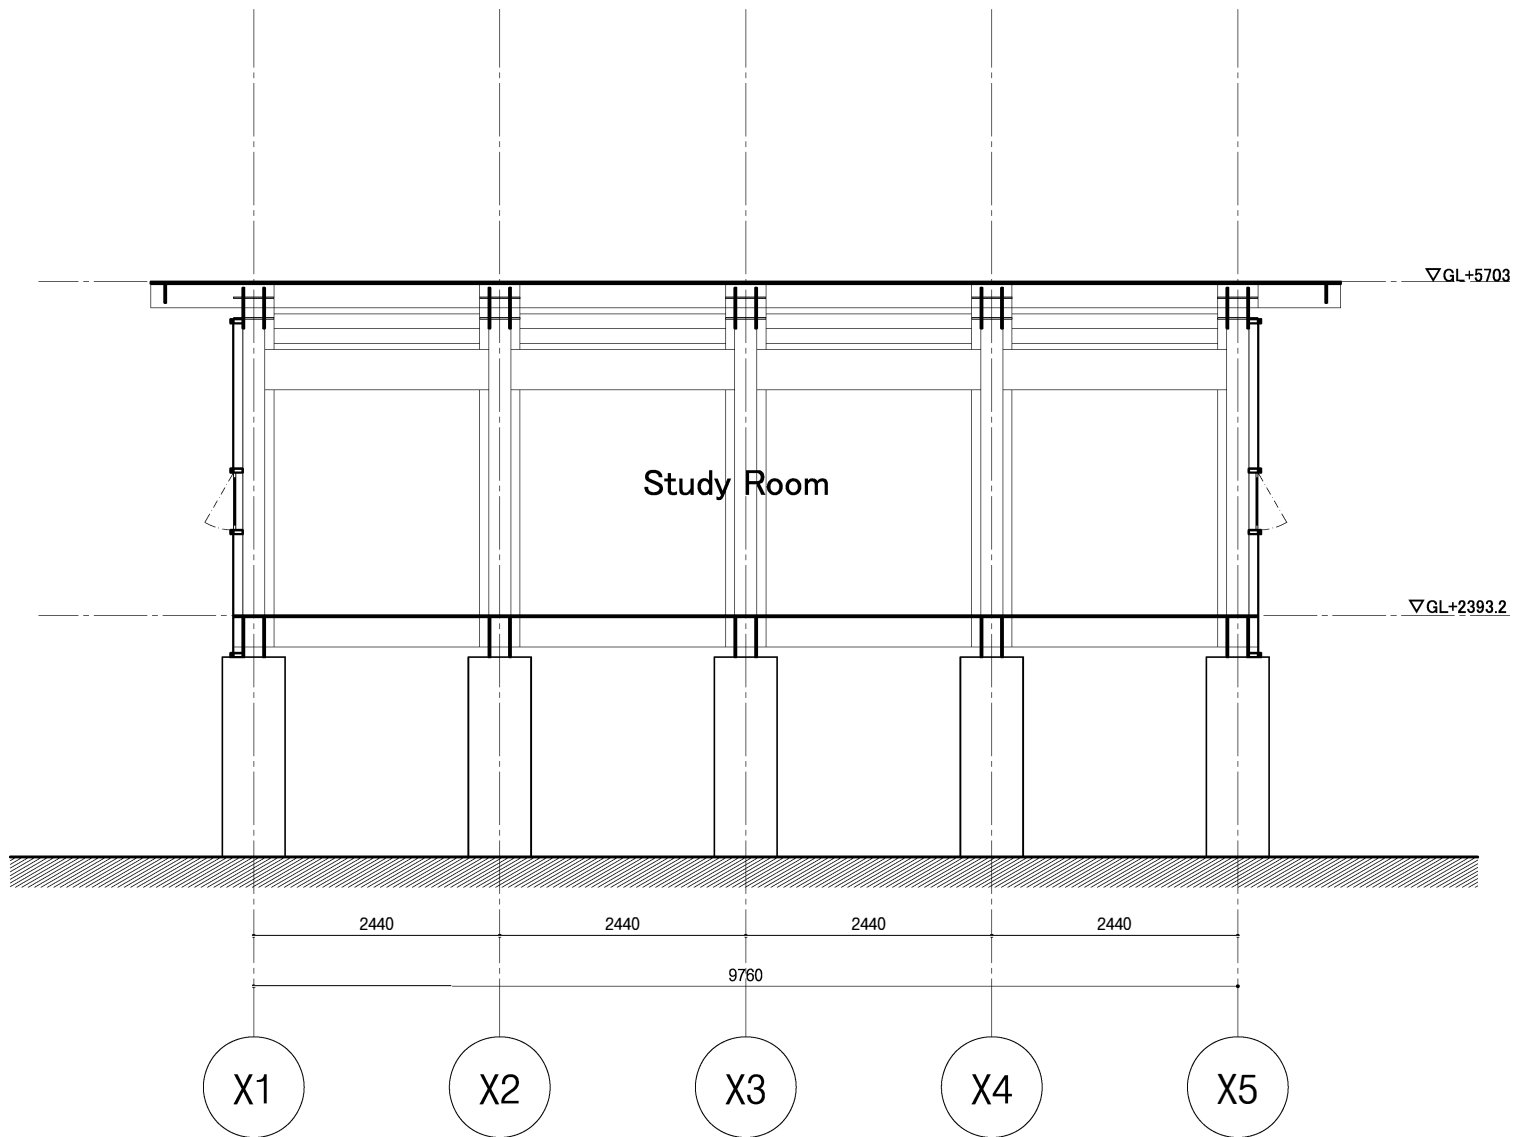

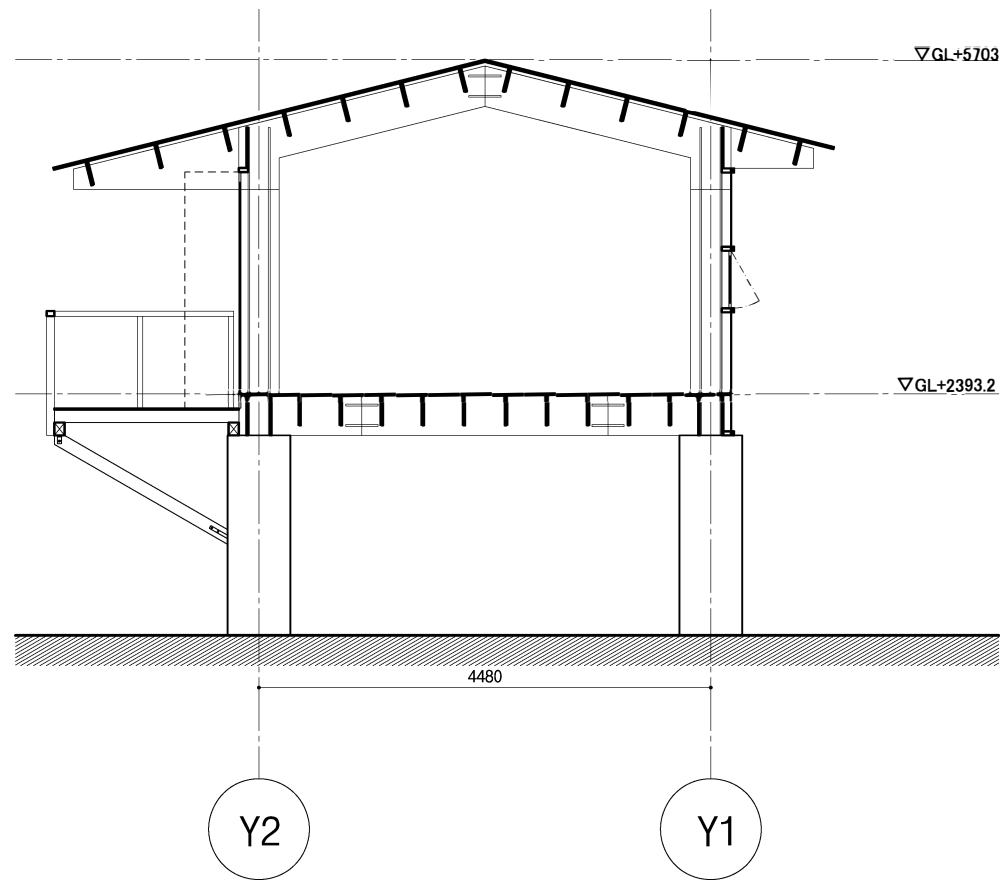


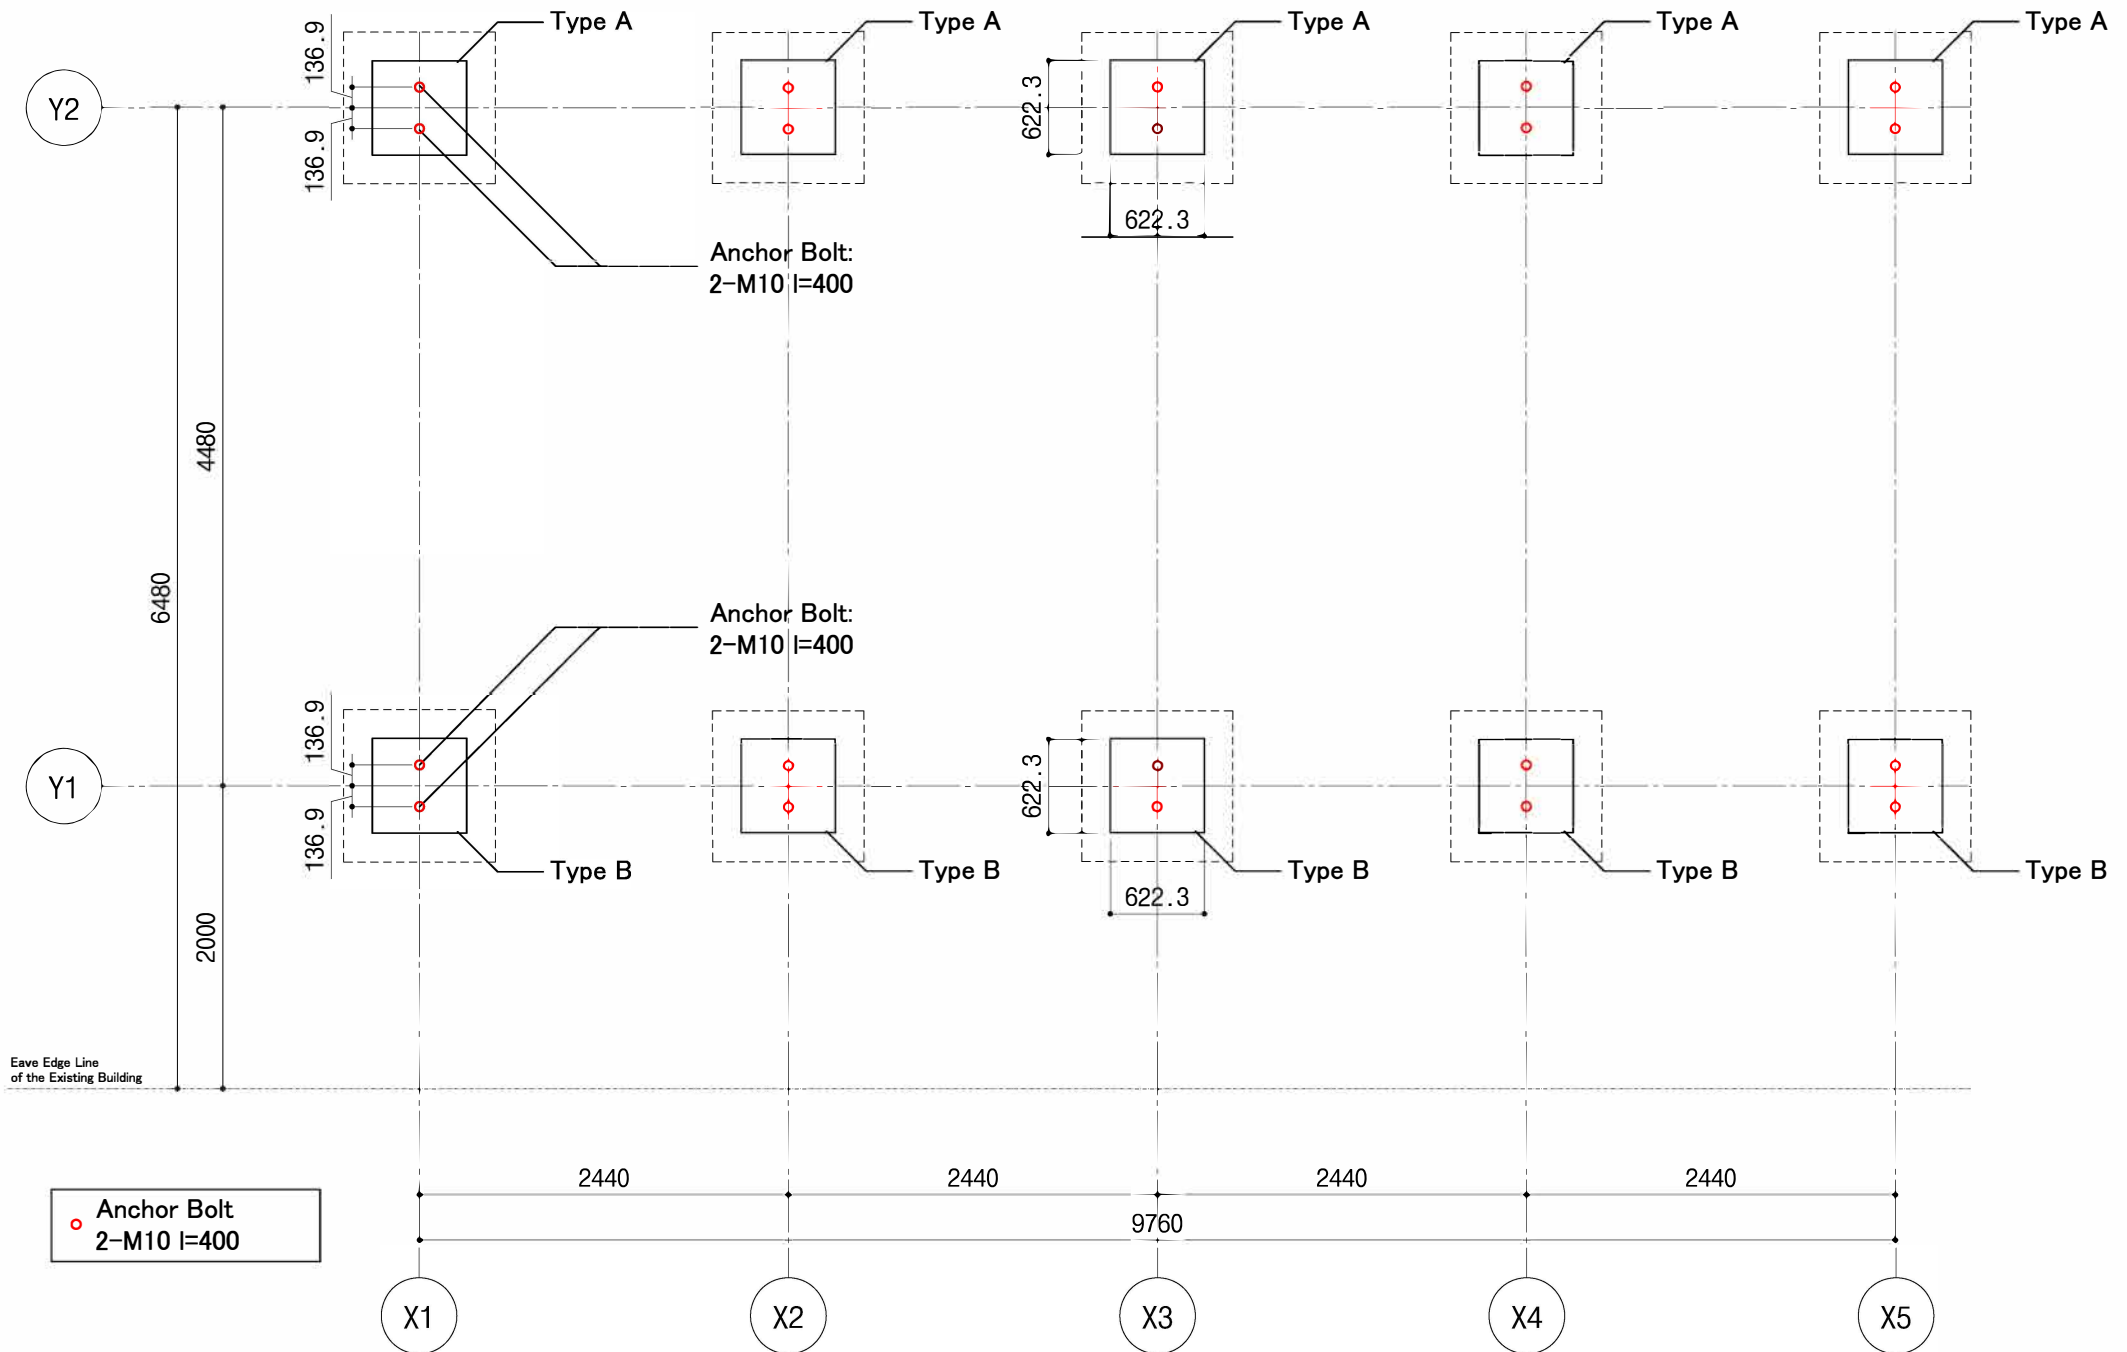


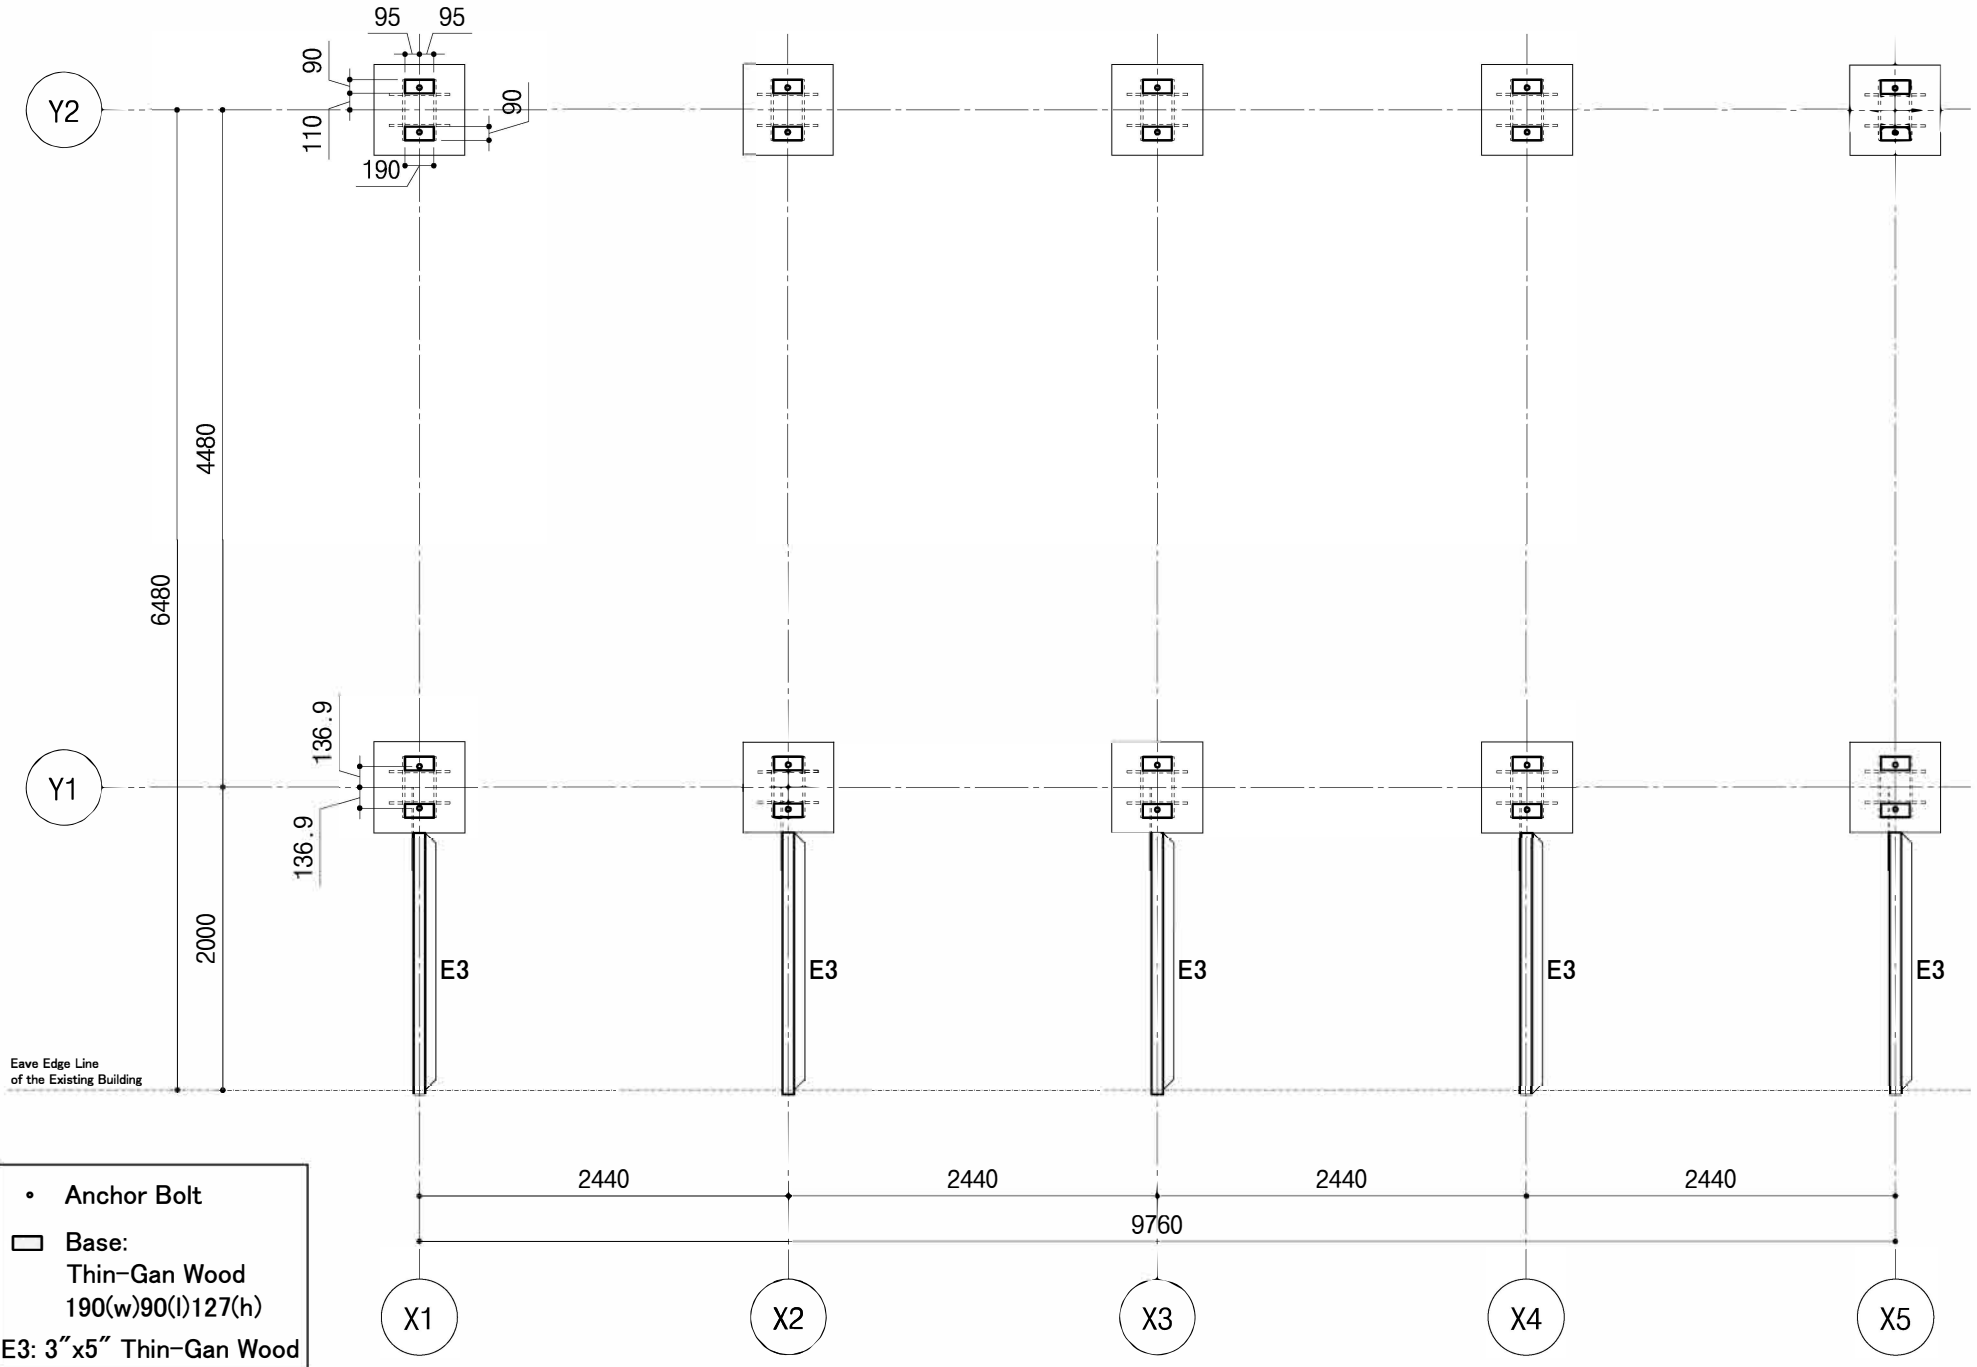


Base Plan

Scale 1:50

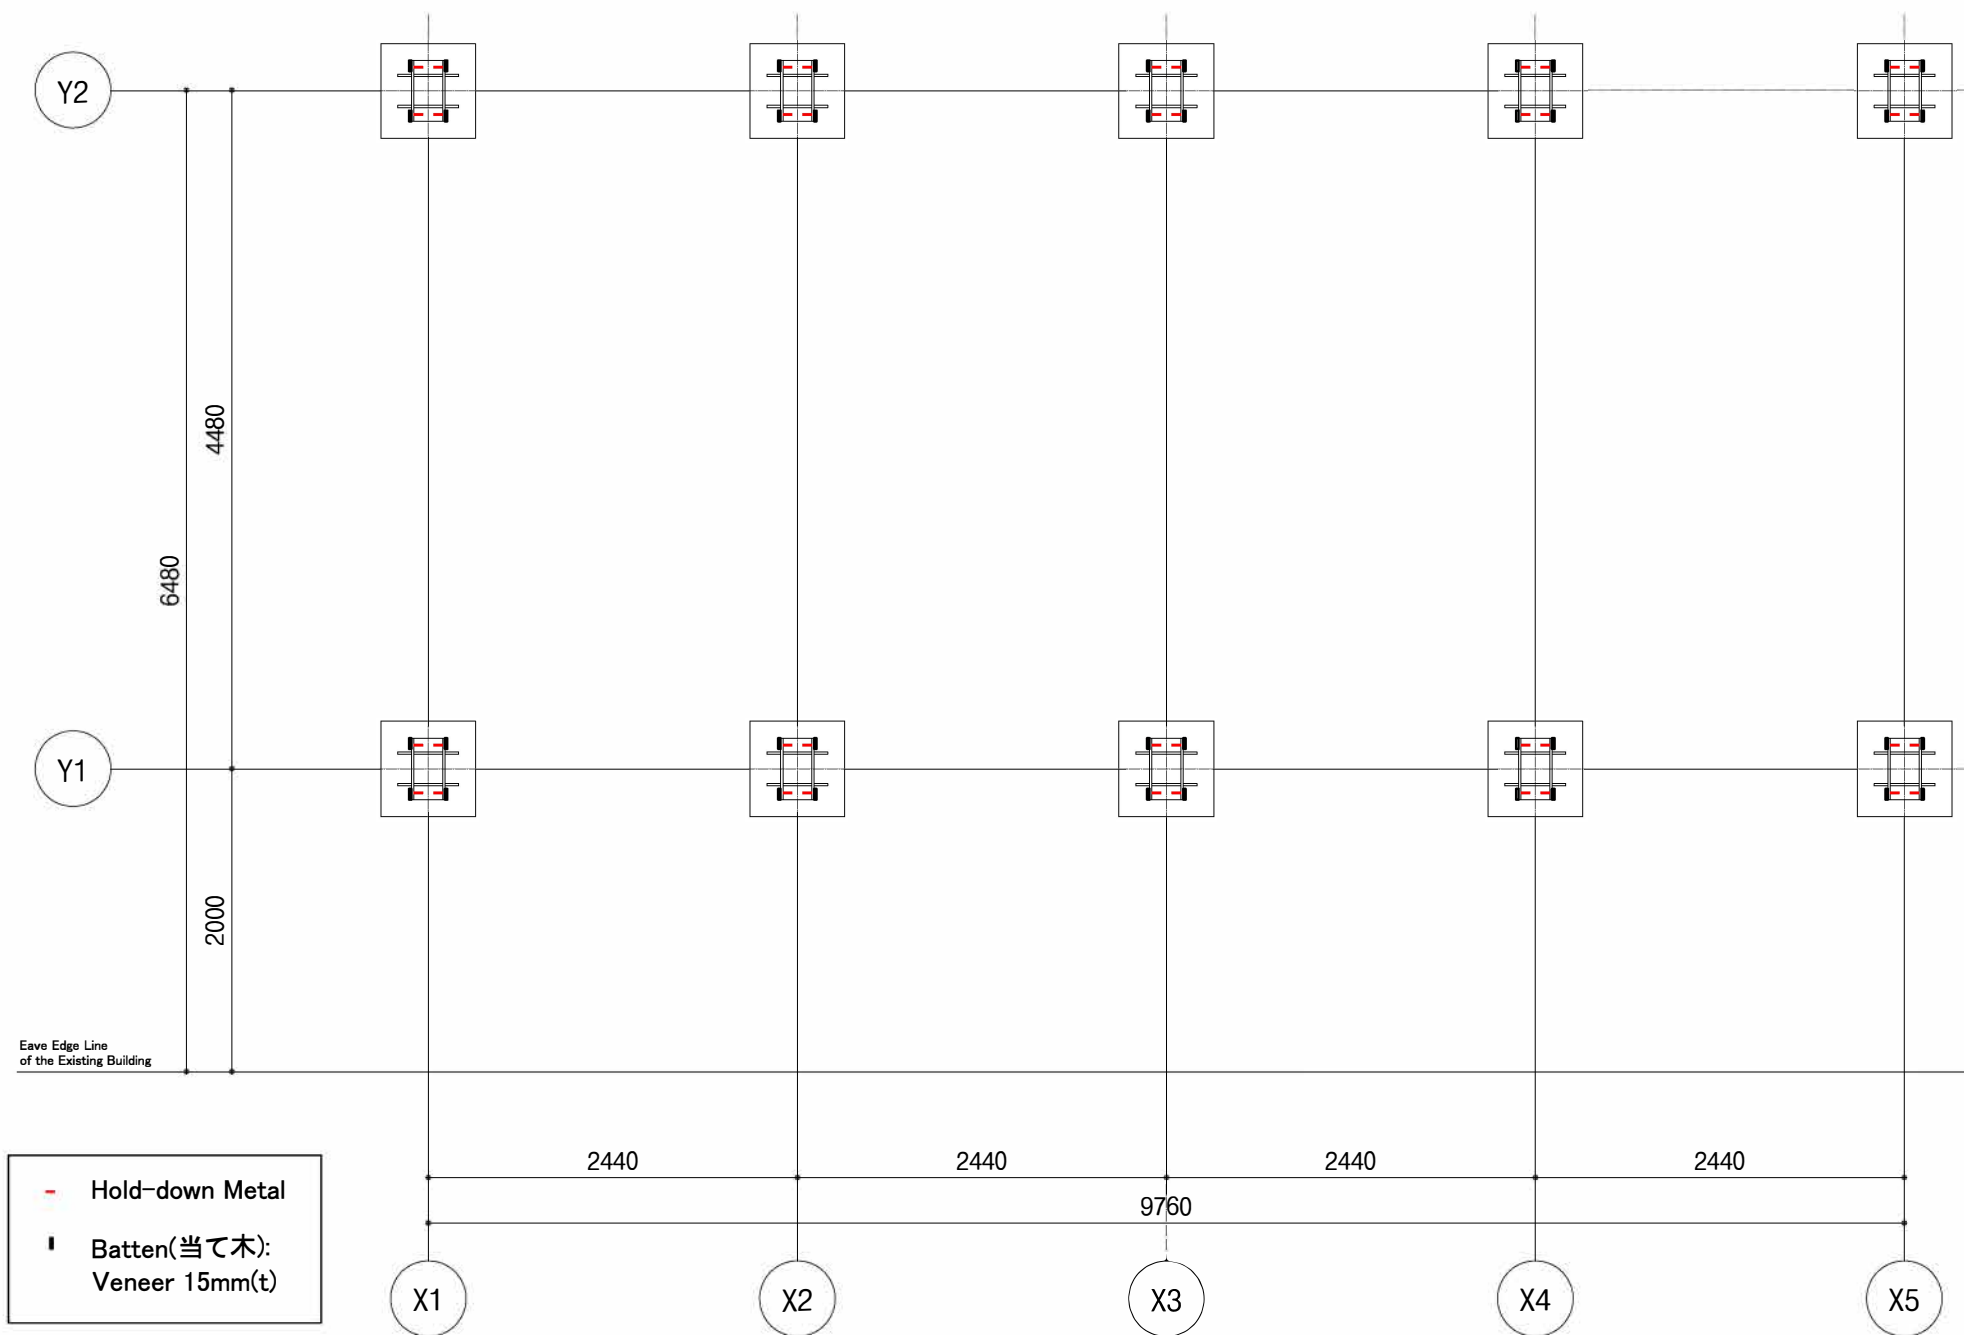

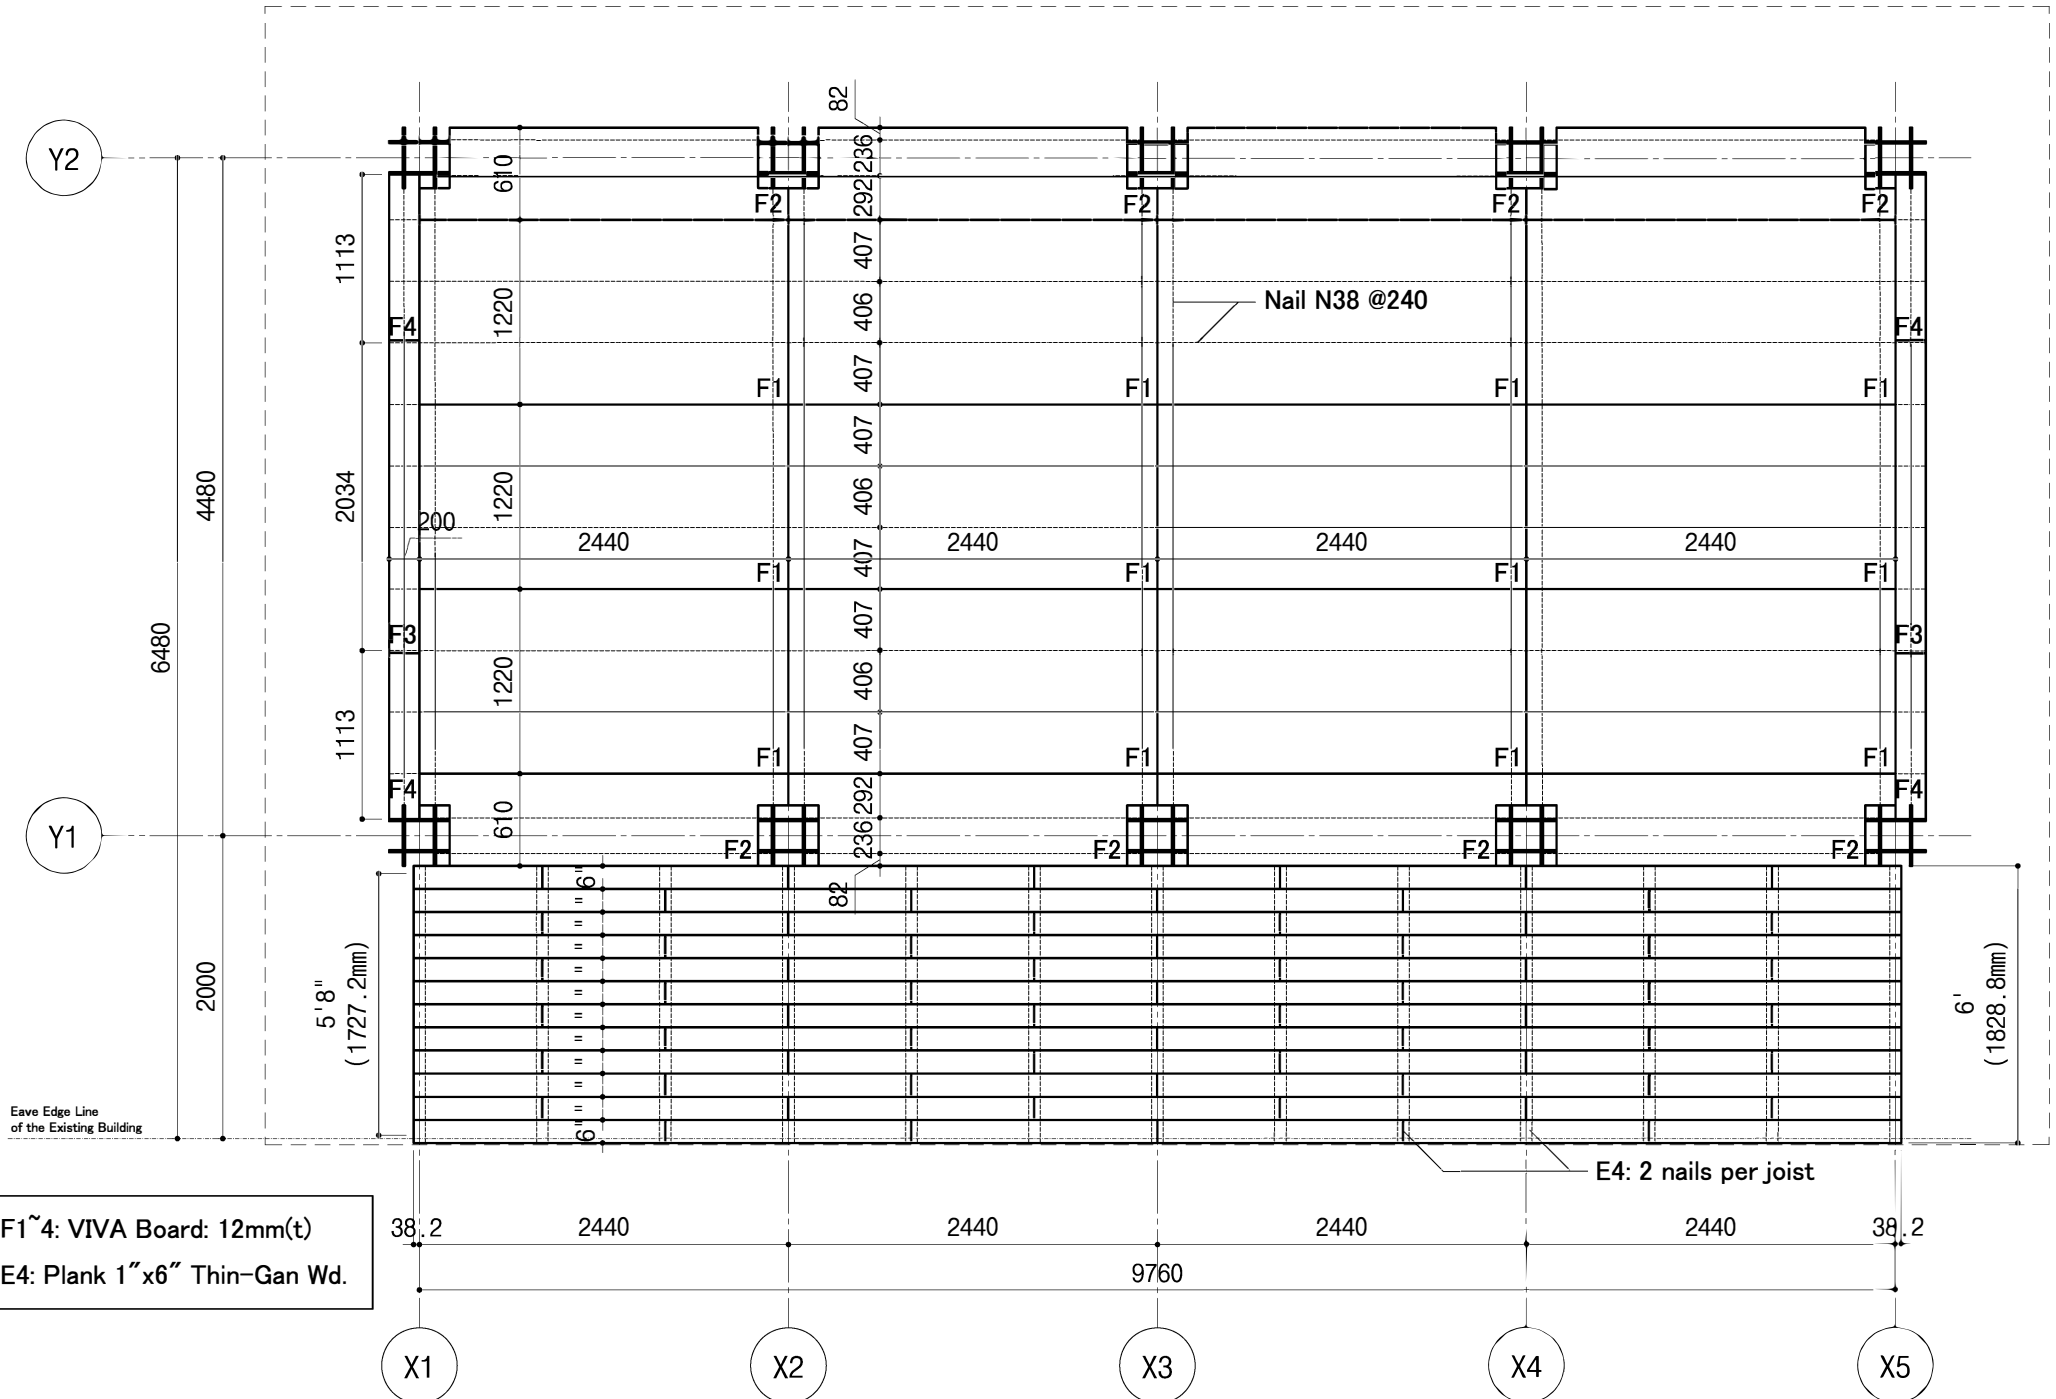

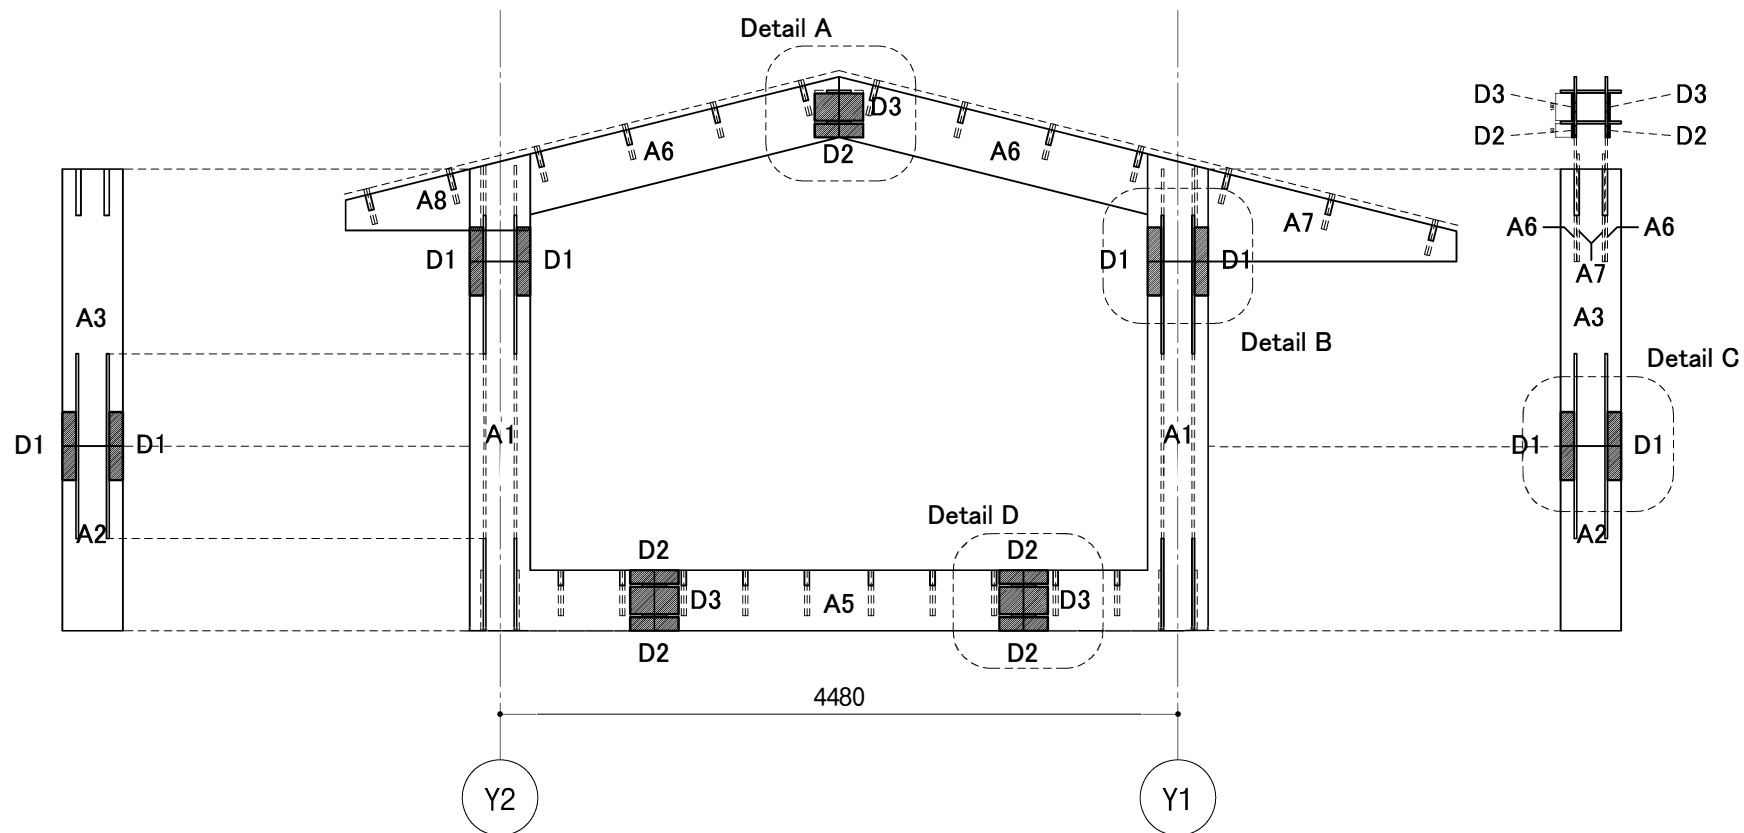


D1: 450(H) 90(L) 15(T)
D2: 320(H) 90(L) 15(T)
D3: 180(H) 320(L) 15(T)


Reinforcement Elevation

※All the veneer thickness is 15mm.




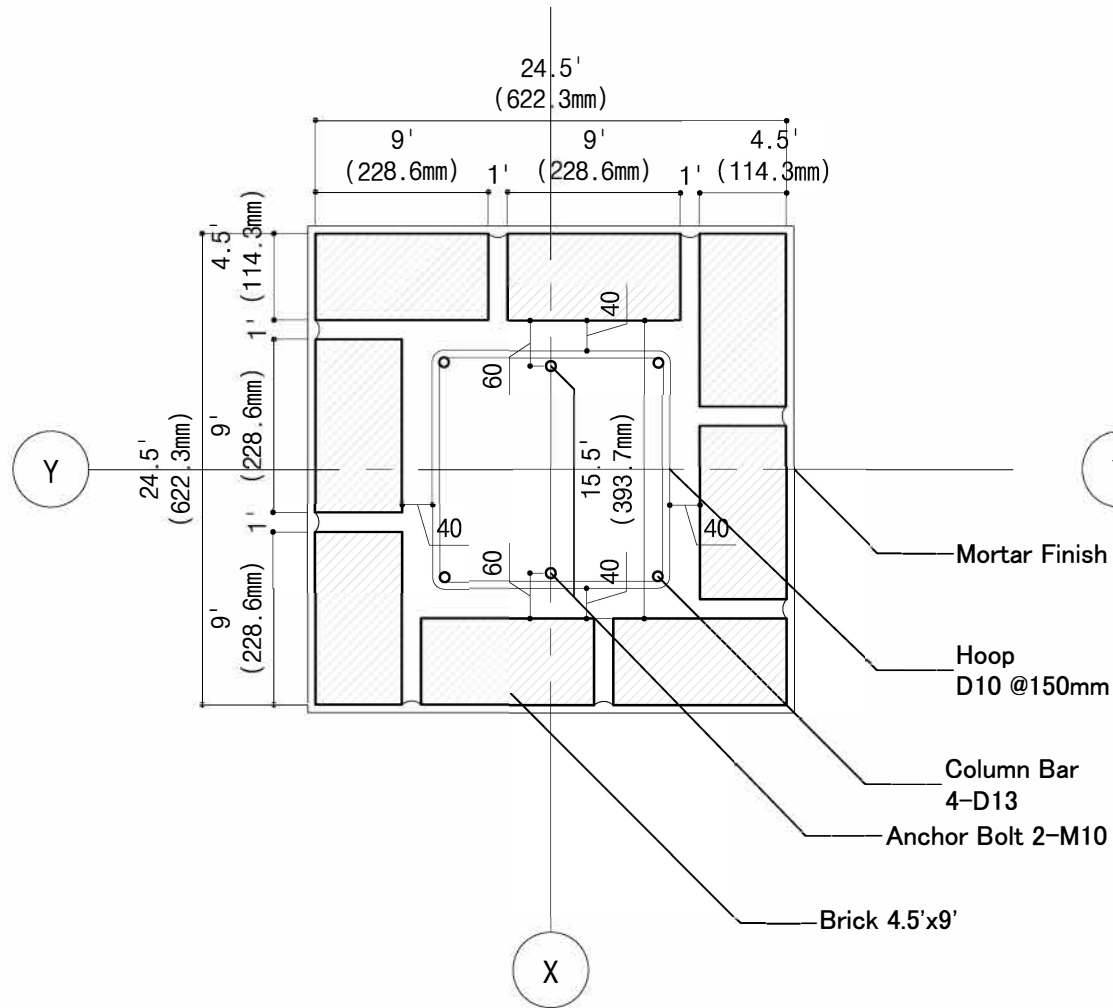

Reinforcement Detail
Type A+B

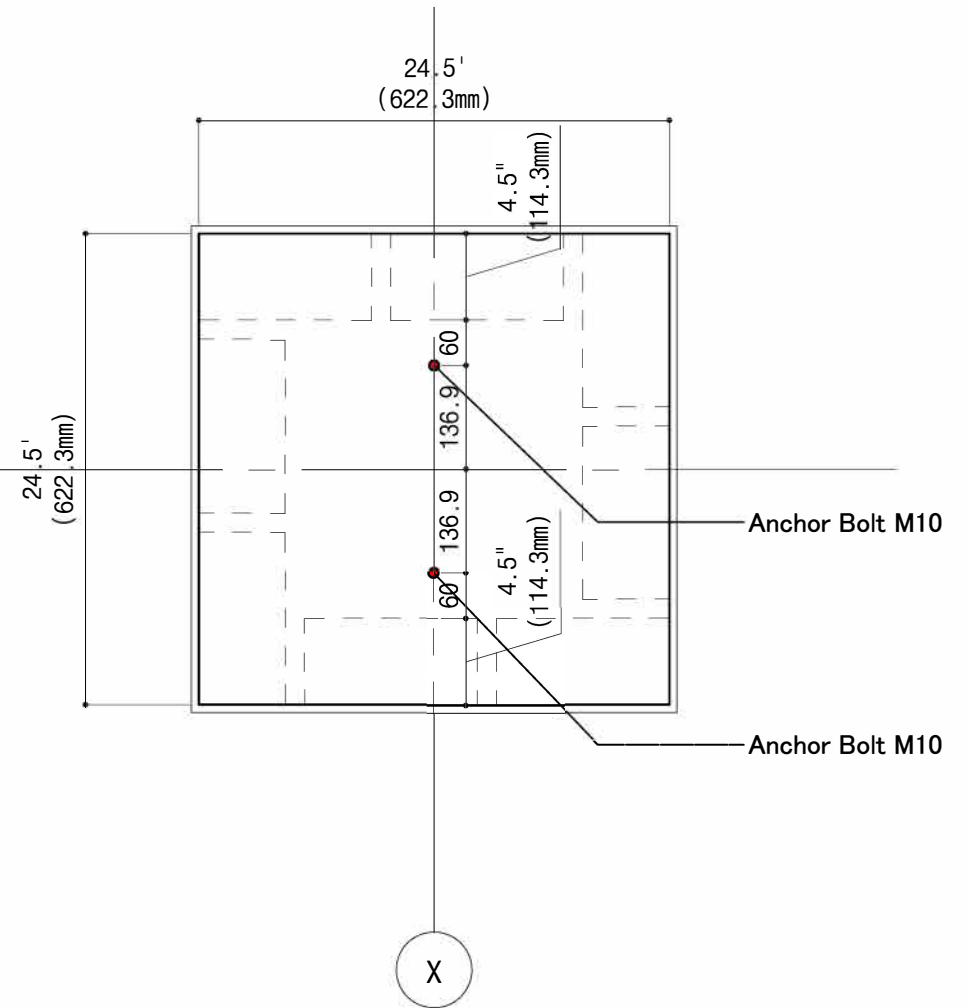


Anchor Bolt Detail
Type A+B

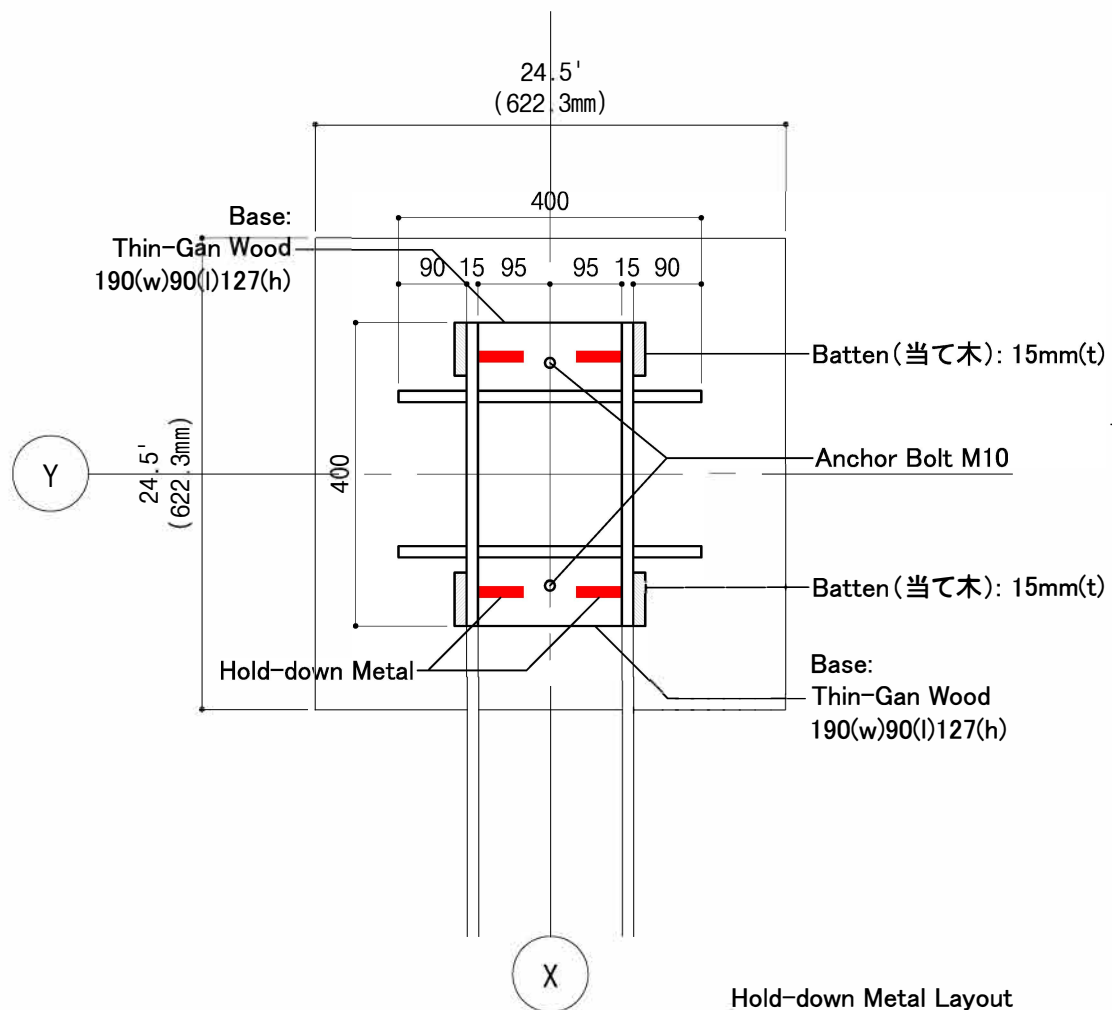

Hold-down Metal Layout
Type A

Hold-down Metal

Batten(当て木): Veneer 15mm(t)

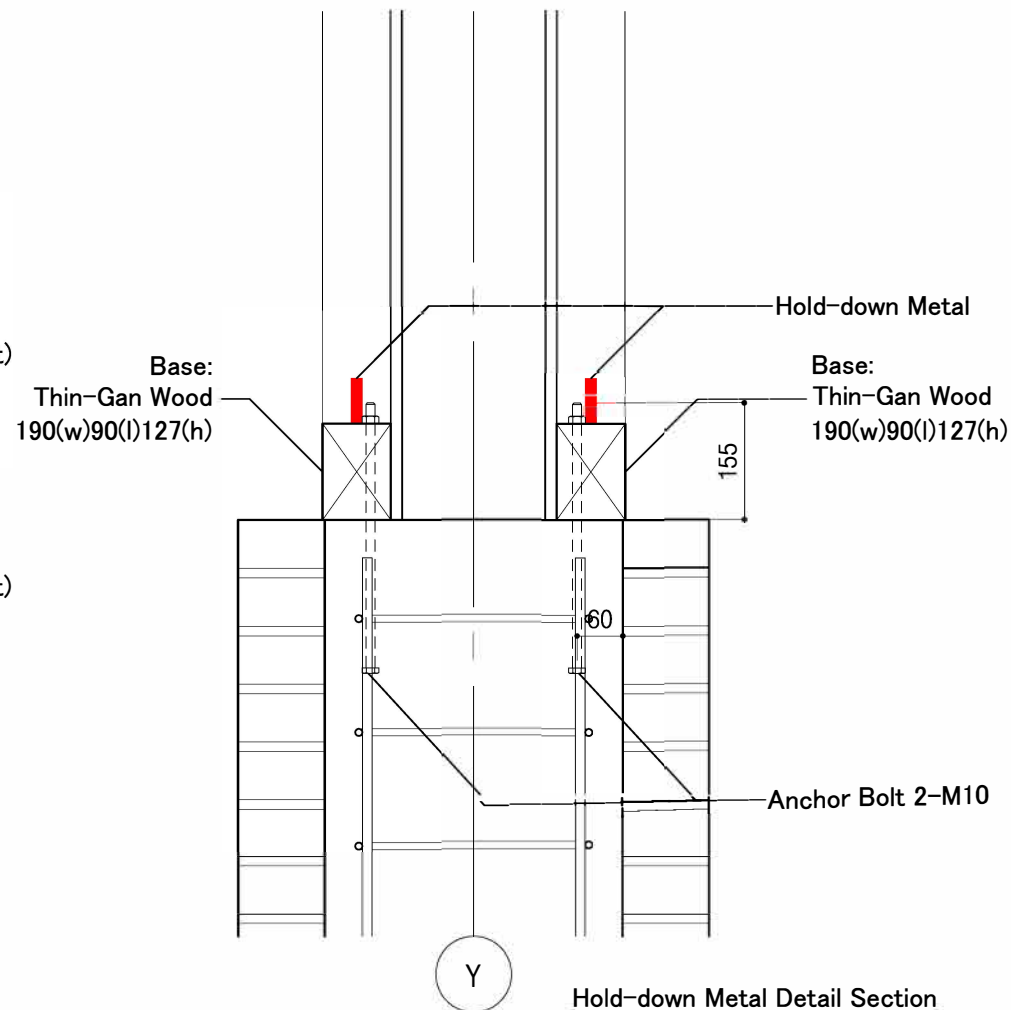

Hold-down Metal Detail Section
Type A

